


Пример расчёта длины по изометрии

LC_1031 Отдельный учебный лист Все размеры на чертеже в миллиметрах

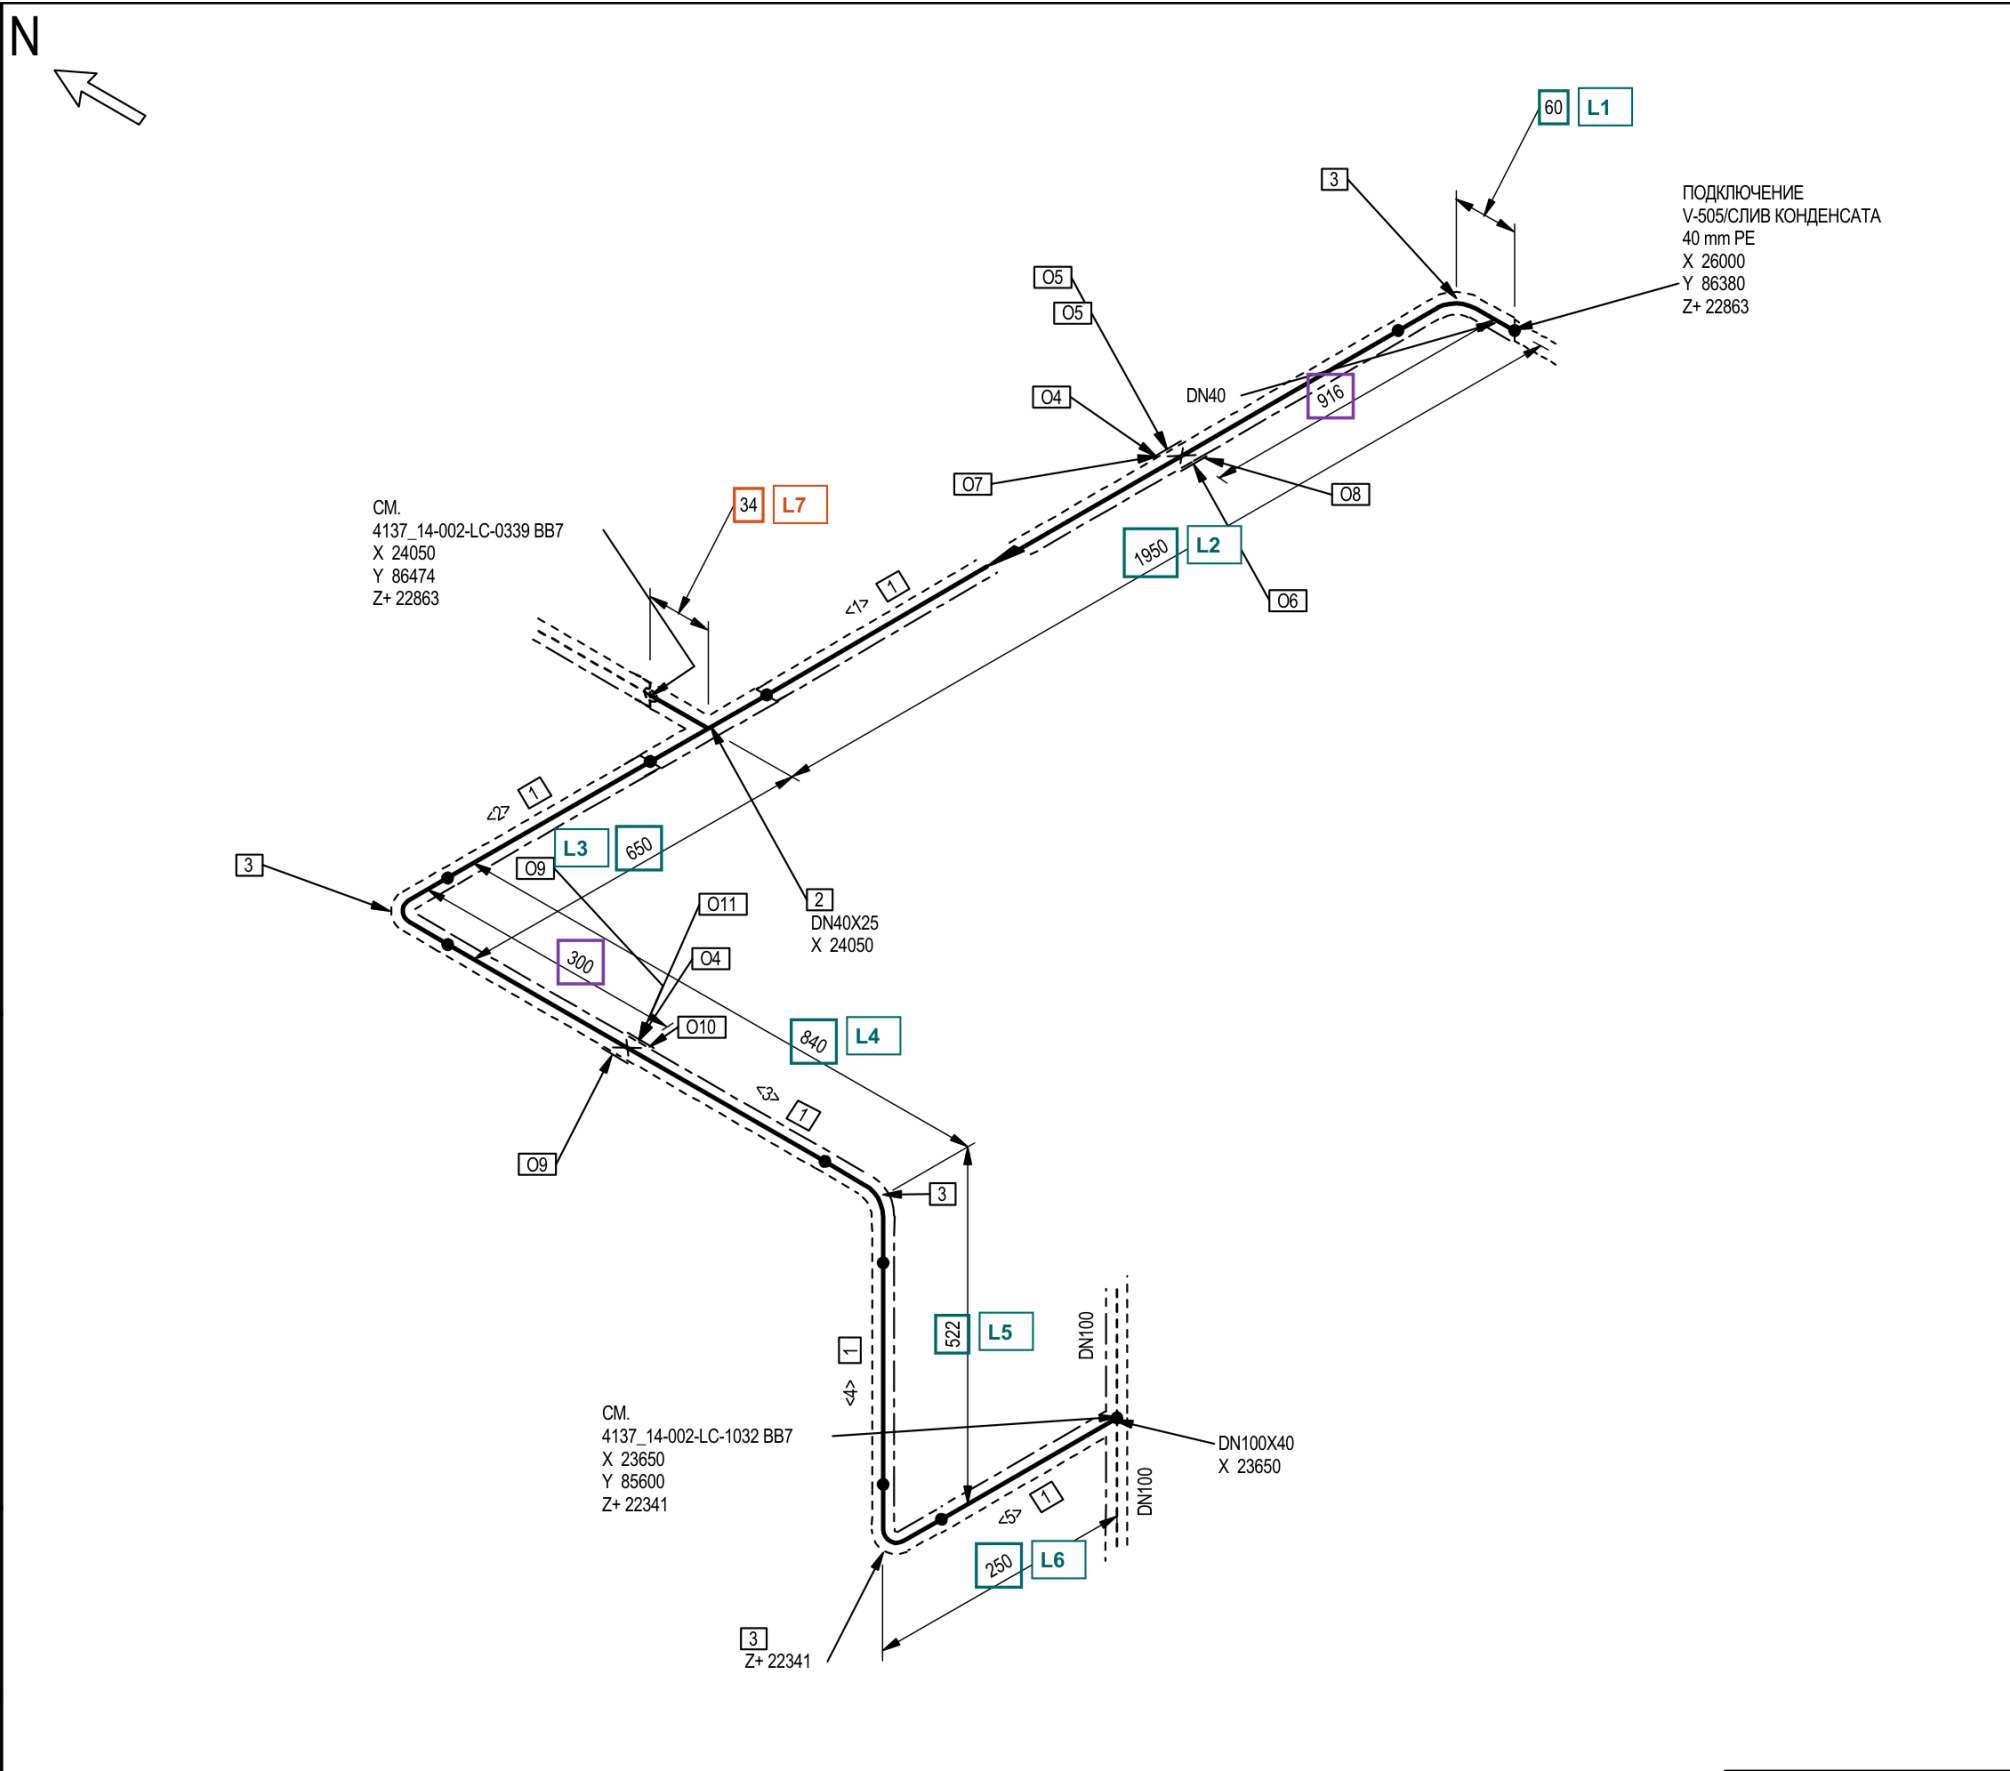

Суммарная размерная длина

4306 мм = 4,306 м

Основная трасса 4272 мм + ветвь 34 мм

Метка	Участок	Размер мм
L1	Основная трасса	60
L2	Основная трасса	1950
L3	Основная трасса	650
L4	Основная трасса	840
L5	Основная трасса	522
L6	Основная трасса	250
L7	Ответвление	34

Основная трасса
 $60 + 1950 + 650 + 840 + 522 + 250 = 4272 \text{ мм.}$

С учётом ответвления
 $4272 + 34 = 4306 \text{ мм} = 4,306 \text{ м.}$

Почему 916 и 300 не прибавляются

Эти размеры задают положения опор внутри участков 1950 и 840 мм. Они уже входят в принятую цепочку. Повторное сложение зависит длину.

- L1–L6 — размеры основной трассы.
- L7 — длина ответвления.
- Фиолетовые рамки — исключённые вложенные размеры.